


PB - COBERTURA

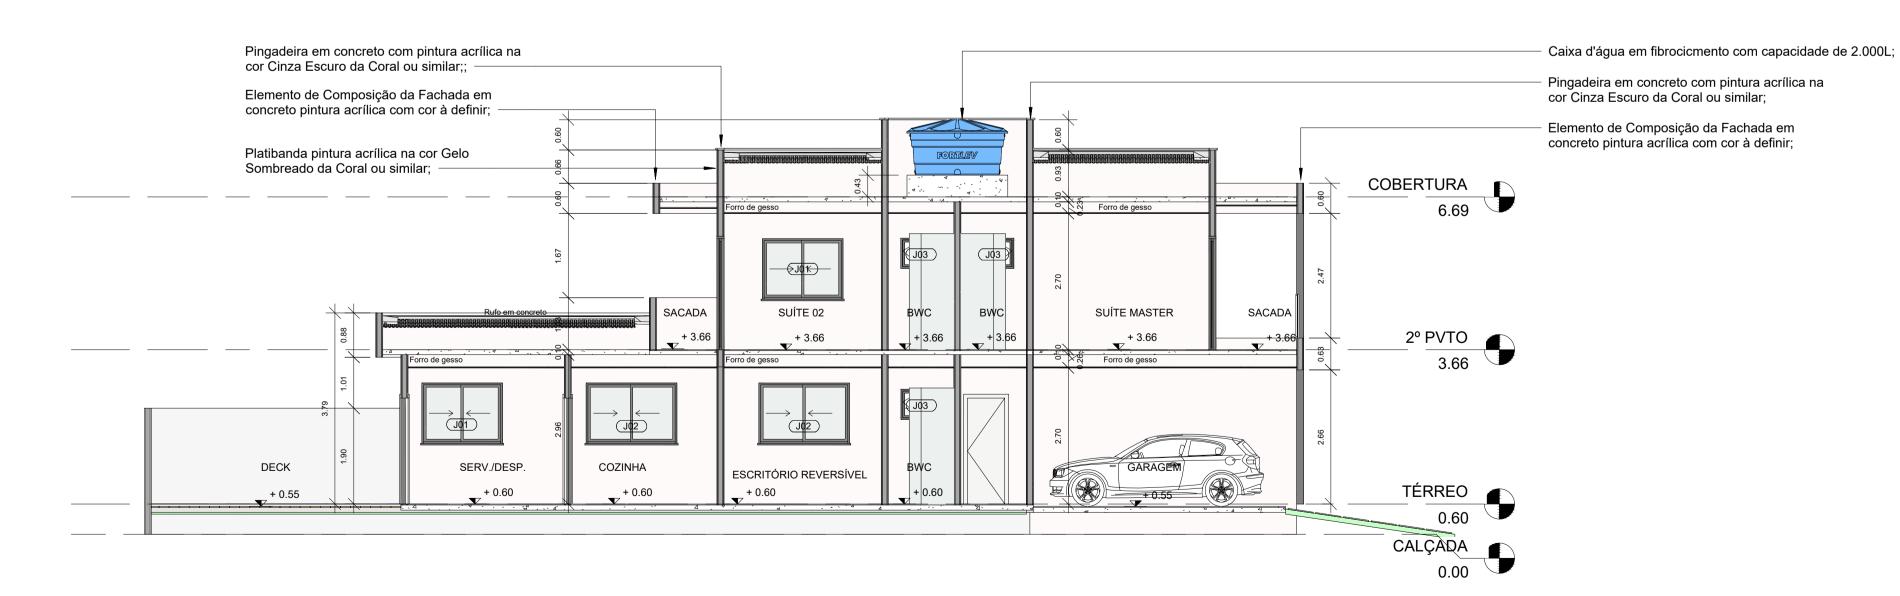

2 CORTE AA 1:75

ESPECIFICAÇÃO DE REVESTIMENTOS E ACABAMENTOS

- P1 Piso em concreto natural; P2 - Piso Porcelanato Acetinado 80x80cm (acabamento à escolher);
- P3 Piso Porcelanato Polido 80x80cm (acabamento à escolher);
- P4 Piso Porcelanato Acetinado 60x60cm (acabamento à escolher); P5 - Piso Mármore Polido (acabamento à escolher);
- P6 Piso Porcelanato Madeirado Deck (acabamento à escolher);
- P7 Grama tipo esmeralda;
- P8 Piso em Pastilha Cerâmica med. 7,5 x 7,5cm brilhante, linha Noronha Mar Mash BR da Eliane ou similar; PAREDES:
- R1 Pintura Acrílica na cor Gelo Sombreado da Coral ou similar; R2 Revestimento Tijolo Aparente na cor Terracota (à escolher);
- R3 Porcelanato 30x60cm (acabamento à escolher); R4 - Porcelanato Madeirado 20x120cm (acabamento à escolher);
- R5 Pastilha Cerâmica 7,5 x 7,5cm brilhante, linha Noronha Mar mash BR da Eliane ou similar;
- R6 Porcelanato Hexagonal 17x19,5cm (à escolher);

FORROS:

F1 - Forro em Gesso Acartonado pintura fosca Branco Neve da Coral ou similar;

RODAPÉS:

- X Rodapé no mesmo Porcelanato do piso h=10cm;
- Z Rodapés em poliestireno branco da Santa Luzia ou similar;

ESPECIFICAÇÃO DE PORTAS E JANELAS

| CÓD. | DIMENSÕES | | | ESPECIFICAÇÃO | | QTDE |
|------|-----------|------|-------|---|----------|------|
| | LARG | ALT | PEIT. | 201 2011 107137.10 | | |
| PV1 | 1.80 | 4.60 | 0.70 | PELE DE VIDRO COM SISTEMA DE FECHAMENTO STICK COM VIDRO LAMINADO DE 8MM (4+4) INCOLOR, COM ABERTURA TIPO MAXIN AIR | | 02 |
| PV2 | 1.20 | 4.60 | 0.70 | PELE DE VIDRO COM SISTEMA DE FECHAMENTO STICK COM VIDRO LAMINADO DE 8MM (4+4) INCOLOR, COM ABERTURA TIPO MAXIN AIR | FIXA | 01 |
| J01 | 1.60 | 1.20 | 1.10 | JANELA DUAS FOLHAS EM VIDRO TEMPERADO INCOLOR 6MM. | CORRER | 04 |
| J02 | 1.80 | 1.20 | 1.10 | JANELA DUAS FOLHAS EM VIDRO TEMPERADO INCOLOR 6MM. | CORRER | 01 |
| J03 | 0.80 | 0.60 | 1.80 | JANELA EM VIDRO TEMPERADO INCOLOR 6MM. | | 04 |
| J04 | 0.50 | 0.50 | 1.80 | JANELA EM VIDRO TEMPERADO INCOLOR 6MM. | MAXIN AR | 01 |
| J05 | 1.80 | 0.40 | 1.80 | JANELA EM VIDRO TEMPERADO INCOLOR 6MM. | MAXIN AR | 01 |
| J06 | 0.80 | 1.20 | 1.10 | JANELA EM VIDRO TEMPERADO INCOLOR 6MM. | MAXIN AR | 01 |
| PT1 | 1.80 | 2.20 | - | PORTA EM DUAS FOLHAS EM VIDRO TEMPERADO INCOLOR 8MM. | | 02 |
| PT2 | 2.00 | 2.20 | - | PORTA EM DUAS FOLHAS EM VIDRO TEMPERADO INCOLOR 8MM. | | 01 |
| PT3 | 2.40 | 2.20 | - | PORTA EM QUATRO FOLHAS EM VIDRO TEMPERADO INCOLOR 8MM. | CORRER | 01 |
| PT4 | 2.70 | 2.20 | - | PORTA EM QUATRO FOLHAS EM VIDRO TEMPERADO INCOLOR 8MM. | CORRER | 01 |
| PM1 | 0.70 | 2.10 | - | PORTA EM MADEIRA LISA PINTADA NA COR BRANCA. | GIRO | 01 |
| PM2 | 0.80 | 2.10 | - | PORTA EM MADEIRA LISA PINTADA NA COR BRANCA. | GIRO | 05 |
| РМ3 | 0.60 | 2.10 | - | PORTA EM MADEIRA LISA PINTADA NA COR BRANCA. | GIRO | 05 |
| PM4 | 1.26 | 2.40 | - | PORTA EM MADEIRA (ACABAMENTO À ESCOLHER). | PIVÔ | 01 |

OBSERVAÇÃO:

- COTAS EM METROS;
- COTAS DE NÍVEL EM METROS;

| QUADRO RESUMO DE ÁREAS | | | | | | | | |
|------------------------------|-------------------|-------------------------|-------------------------------------|--|--|--|--|--|
| ÁREA TOTAL DO LOTE: 364,00m² | PAVIMENTOS | ÁREAS | LOTE: 304 - QUADRA K | | | | | |
| DECLINO | PAV. TÉRREO | 154,48m² | | | | | | |
| resumo área construída | PAV. SUPERIOR | 74,18m² | ÁREA CONSTRUÍDA | | | | | |
| | TOTAL | 228,66m² | 154,48m² = $42,43%$ | | | | | |
| ÁREA PERMEÁVEL: | PISO INTERTRAVADO | 22,59m² | | | | | | |
| | GRAMA | 125,43m² | , | | | | | |
| RESUMO | PISCINA | 12,50m² | ÁREA PERMEÁVEL 148,02m² = 40,66% | | | | | |
| KESOMO | DECK | 30,07m² | 1.0,02 10,00,0 | | | | | |
| | TOTAL | 190,59m² | | | | | | |
| TAXA DE OCUPAÇÃO (TO): | 42.43% | COFF. DE OCUPAÇÃO (CA): | 0.62 | | | | | |



A1 - 84.10 X 59.40

ED. MIRAI OFFICES, SALA 2102 - UMARIZAL - BELÉM - PA, CNPJ - 04.926.230/0001-37